




(VIEW OF THE EXTERIOR FROM DEGNAN BOULEVARD)



(VIEW OF THE COMMUNITY MUSICAL SHOWCASE ROOM)

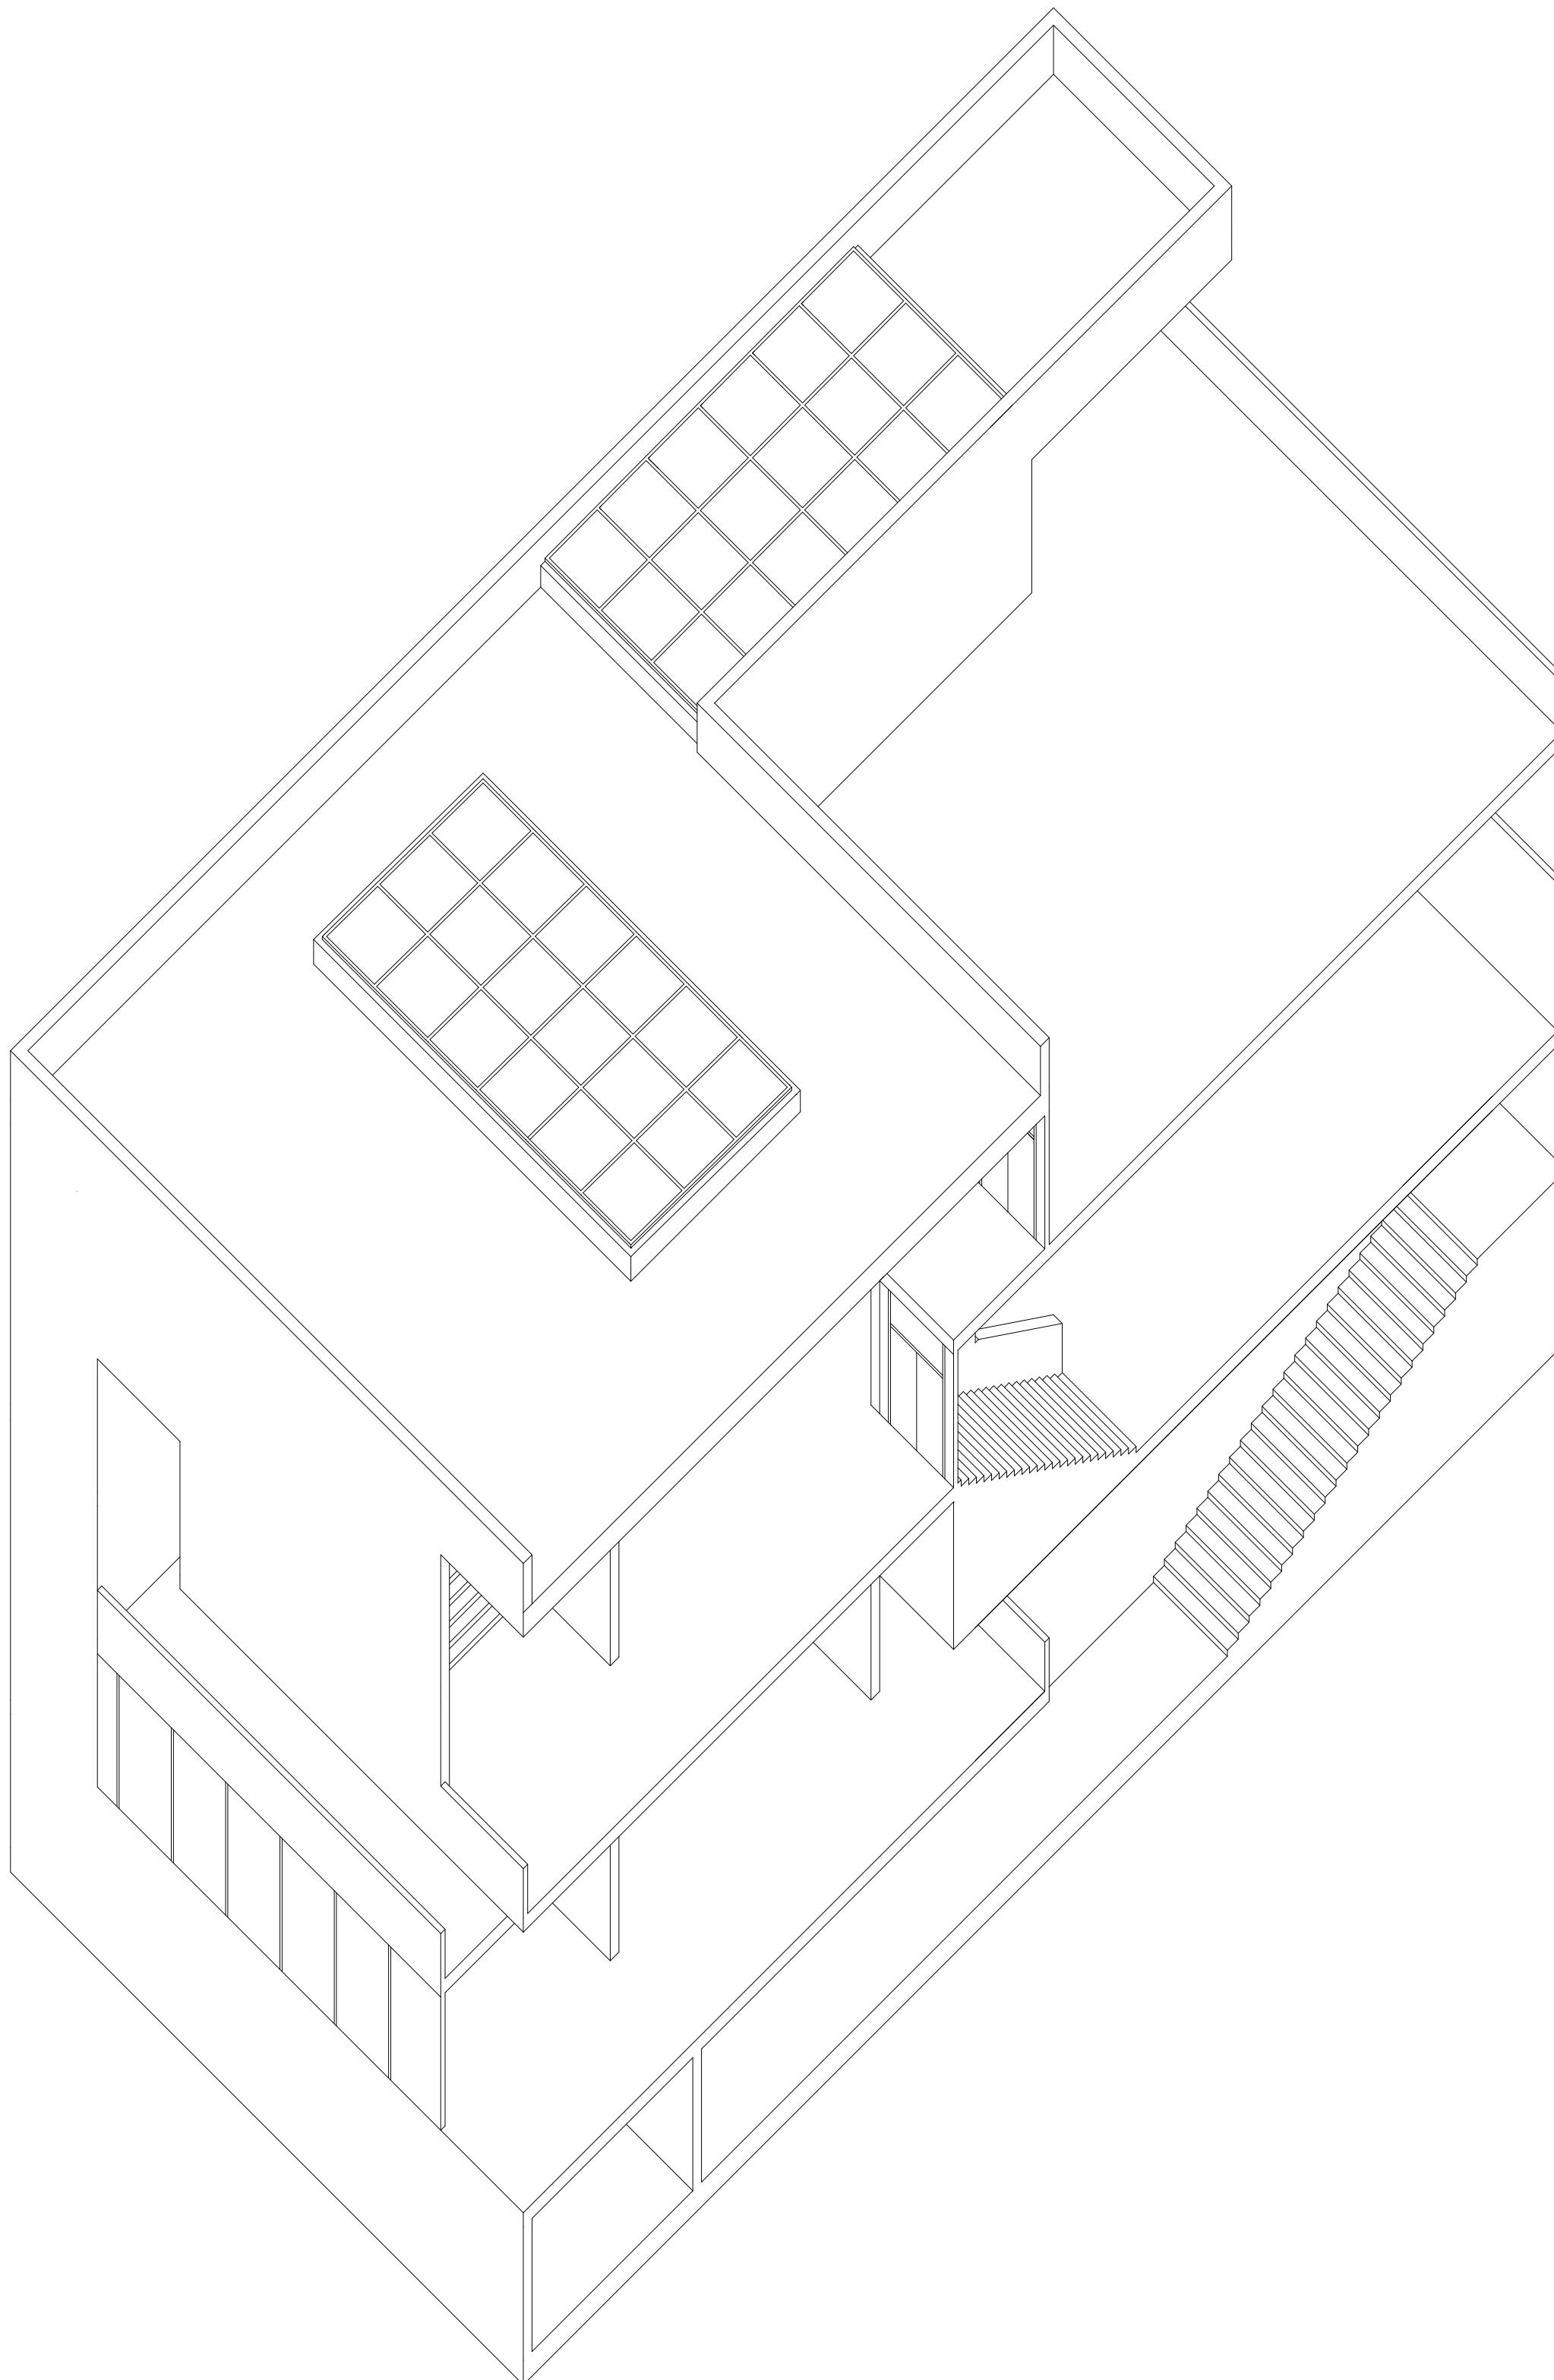


**Adam Bucholtz: Cultural Center of Art, Jazz, and Gardening
Leimert Park, Los Angeles (2023)**

The main idea of this project is exploring the variation of the grid in previous renditions to develop varying spaces, depth, and intrigue. The project utilizes its variety and connects the variations together to form one cohesive through-line with its circulation.


On the first floor users can enter through two main entrances. One accesses the cafe and the other to an information desk that peers into the auditorium below. There is a constant dialogue between outdoor and indoor spaces both with subtracting away from the mass and through glazing. The first floor exemplifies this dialogue. There is circulation between an outdoor patio space and an indoor workspace connected through the cafe and second gallery. The sub level slowly drops below the superstructure leading into a spacious lobby. From the lobby leads into the first gallery which showcases the prominent musical impact of the community. This gallery also is multi-heighted facilitating ample light

and symbolically suggesting the scale of impact of the musical achievements of the community.

Another focus of the proposal is its connection with gardening. Inspired by the Ron Finley Project there is an exterior space on the upper most corner designed to facilitate a potential rooftop gardening space. Its large square footage provides ample room to educate and cultivate and even section off a space if a greenhouse is desired. Many of the spaces that open the elements can be used to house a variety of plant life bringing the earth within and continuing a connection between exterior and interior.

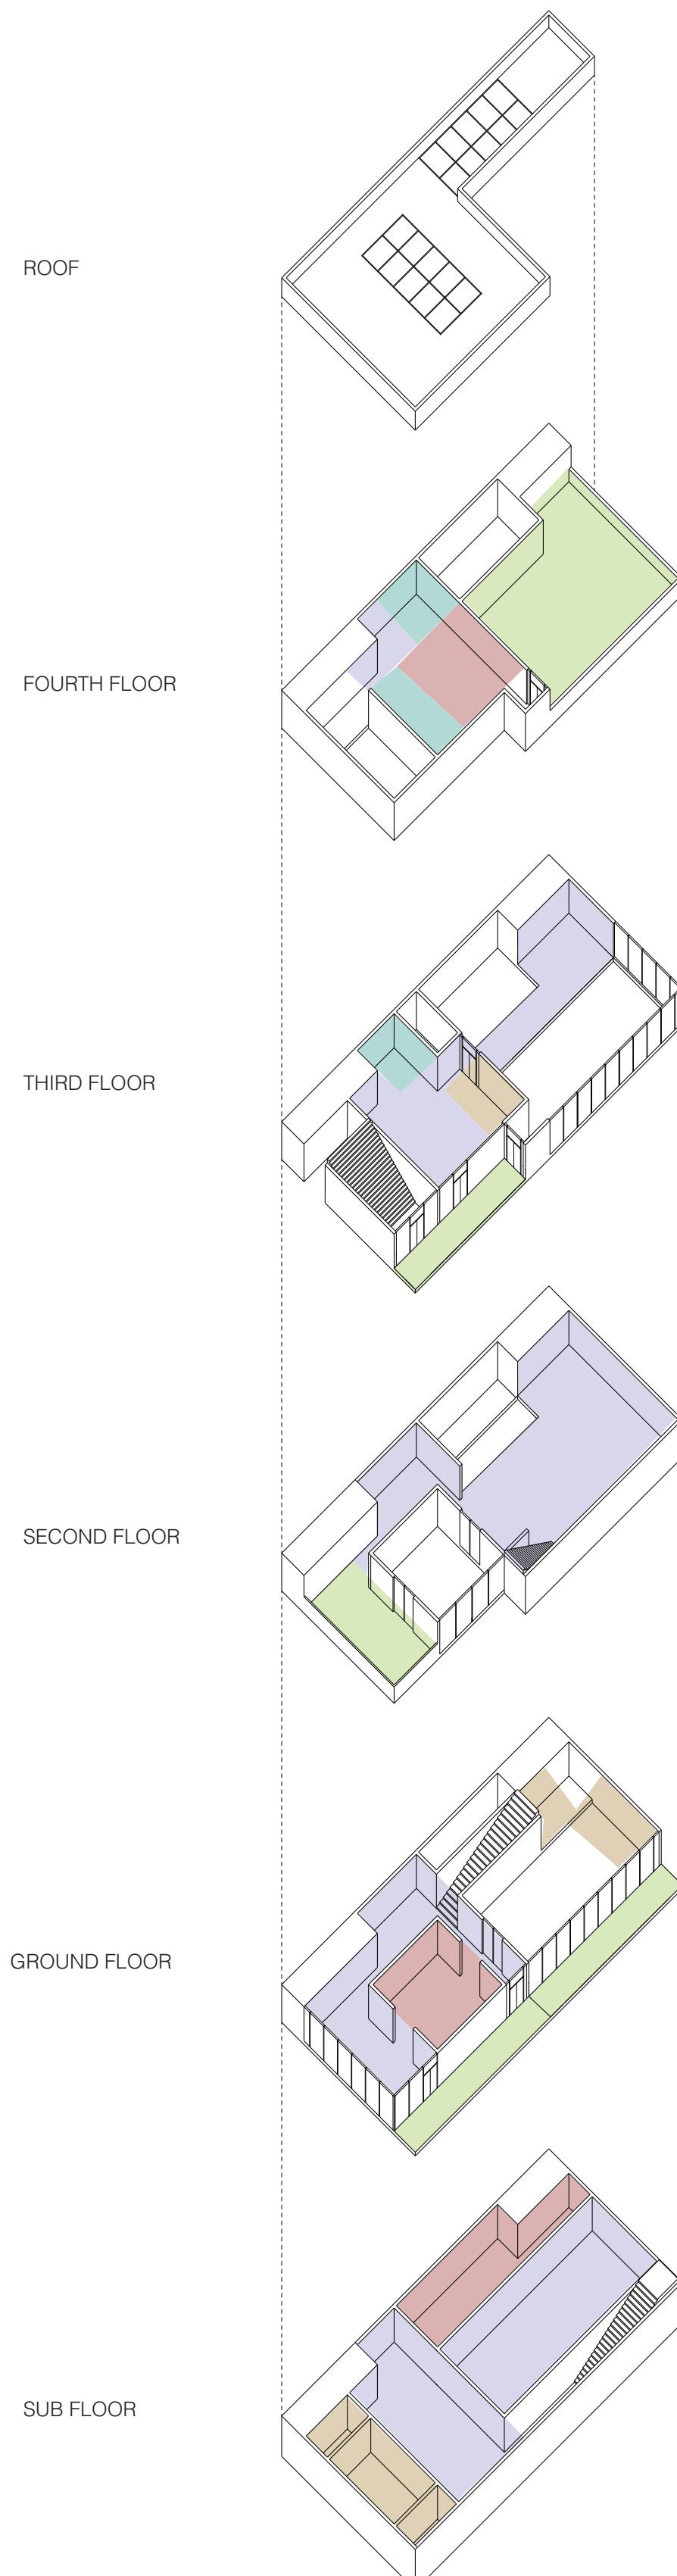



GALLERY
PUBLIC
SUPPORT
EXTERIOR
STAFF


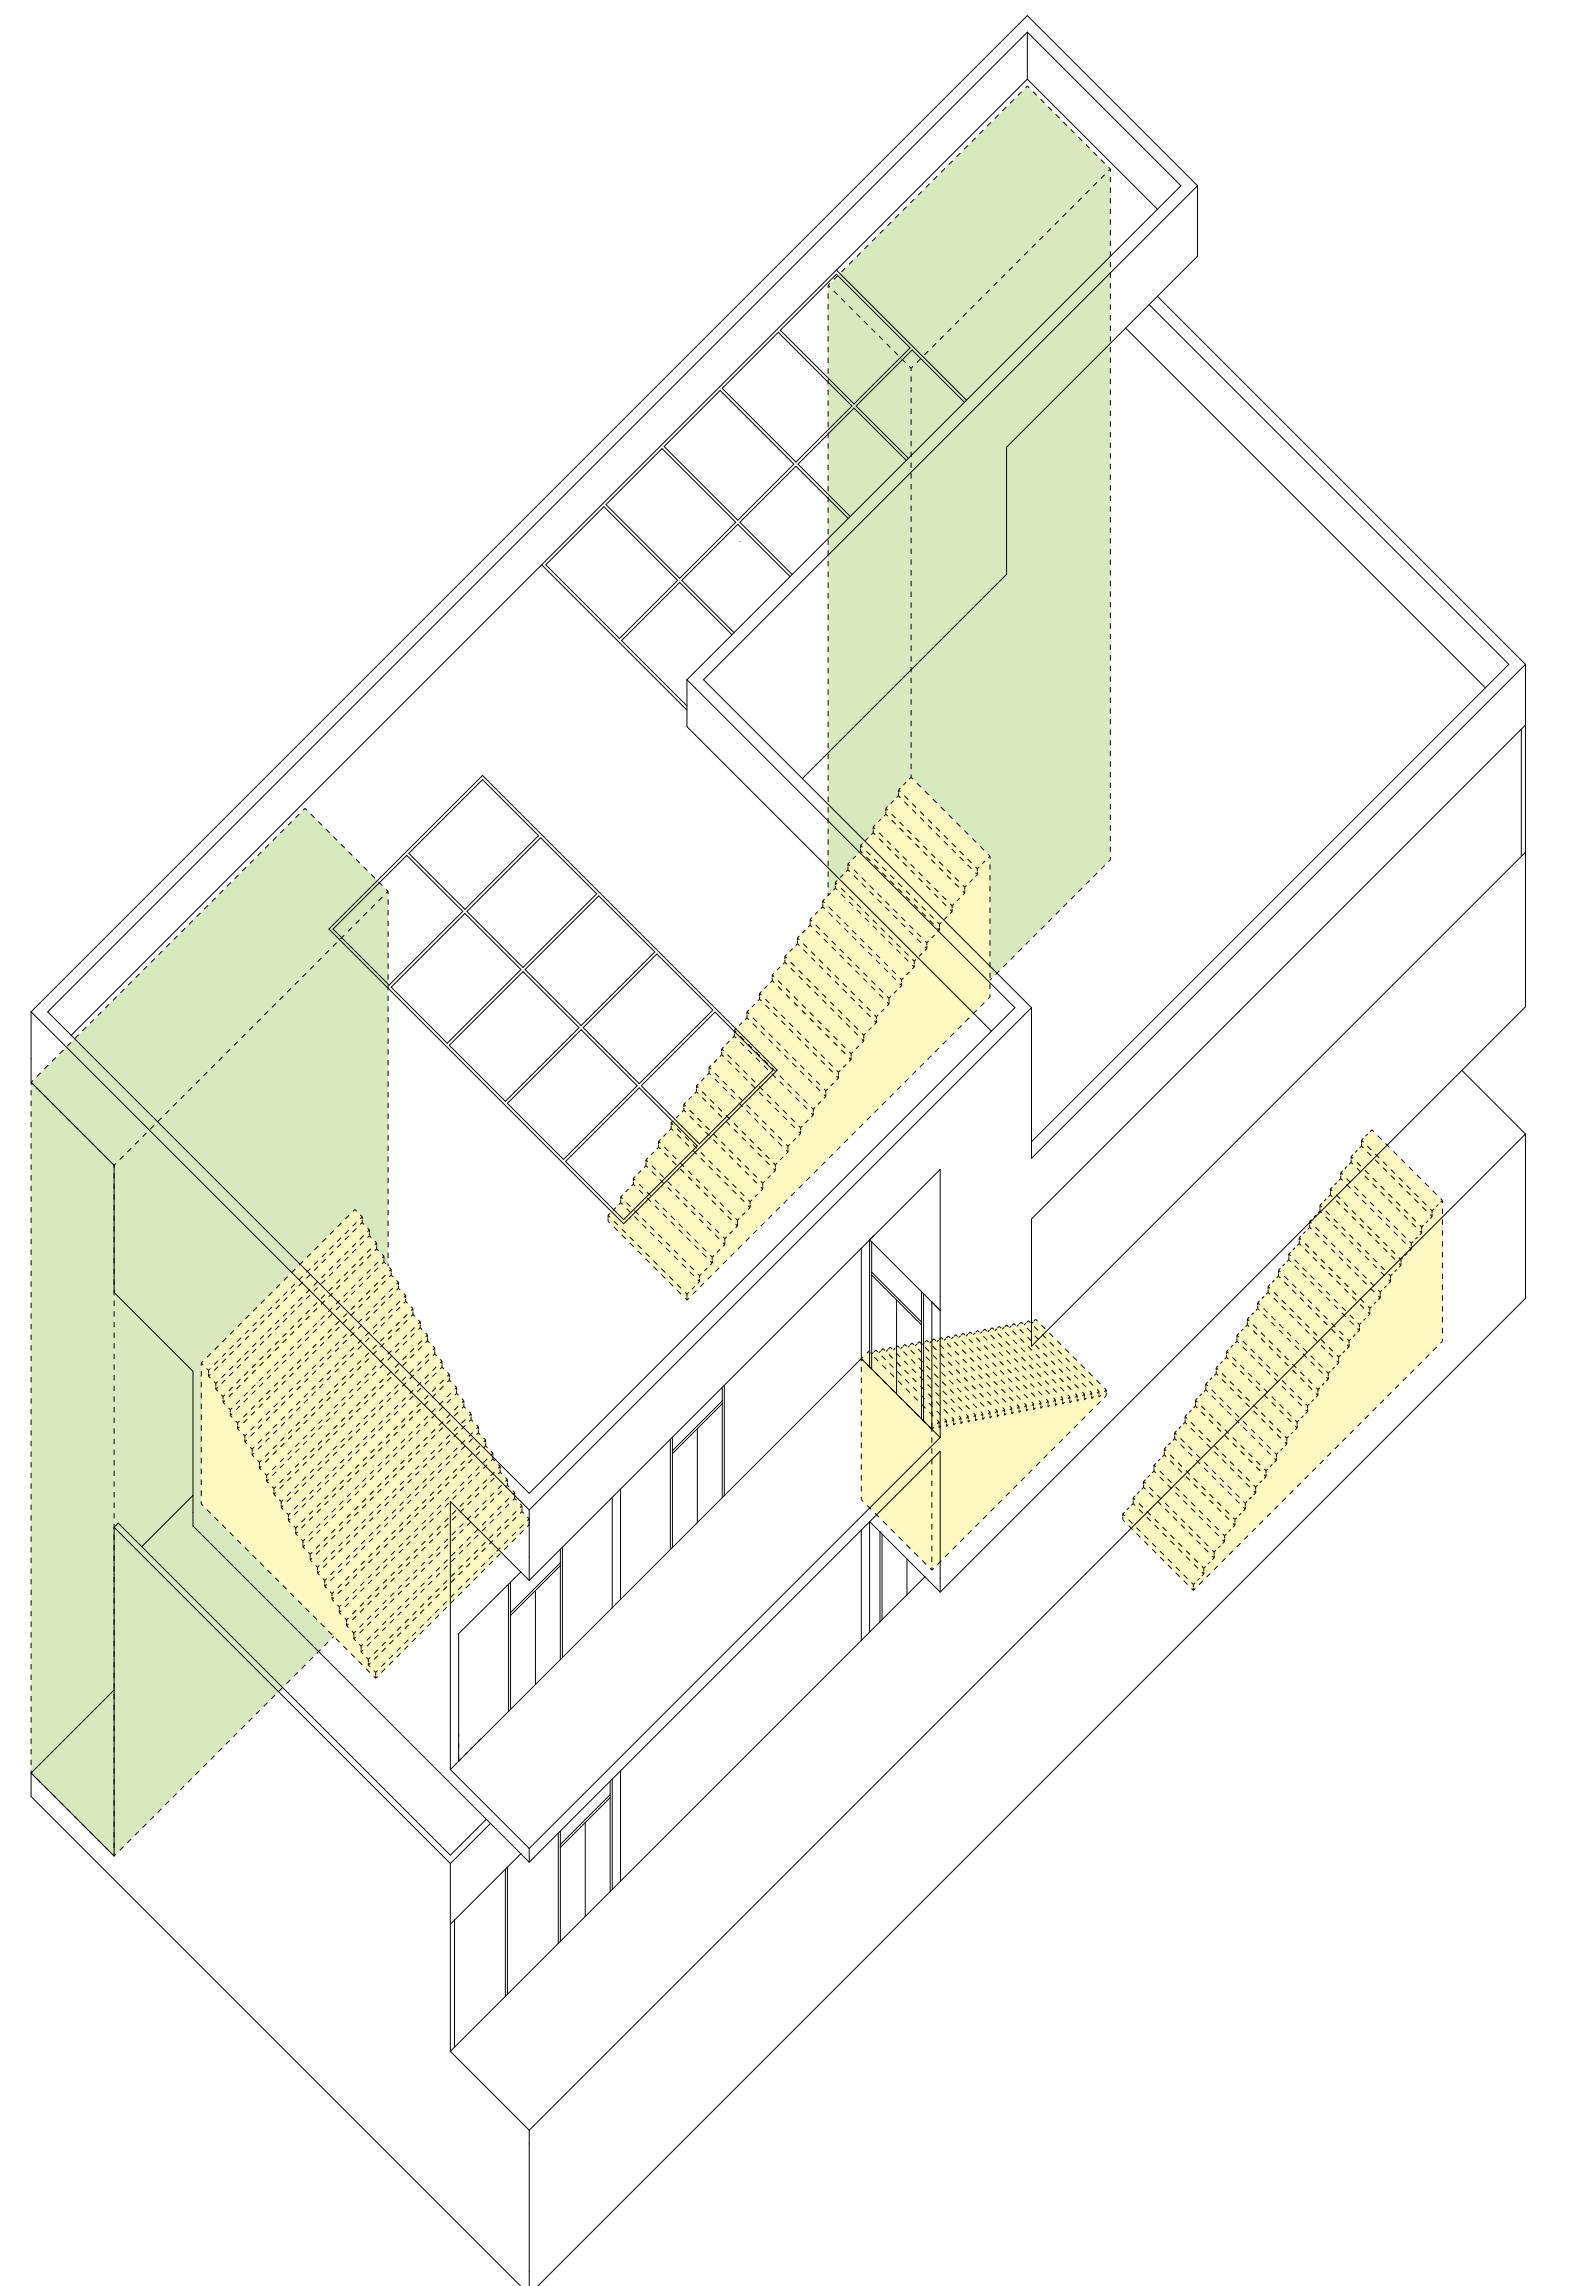



EGRESS CORES
MAIN STAIRS

PROGRAM DIAGRAM
NOT TO SCALE

CIRCULATION DIAGRAM
NOT TO SCALE

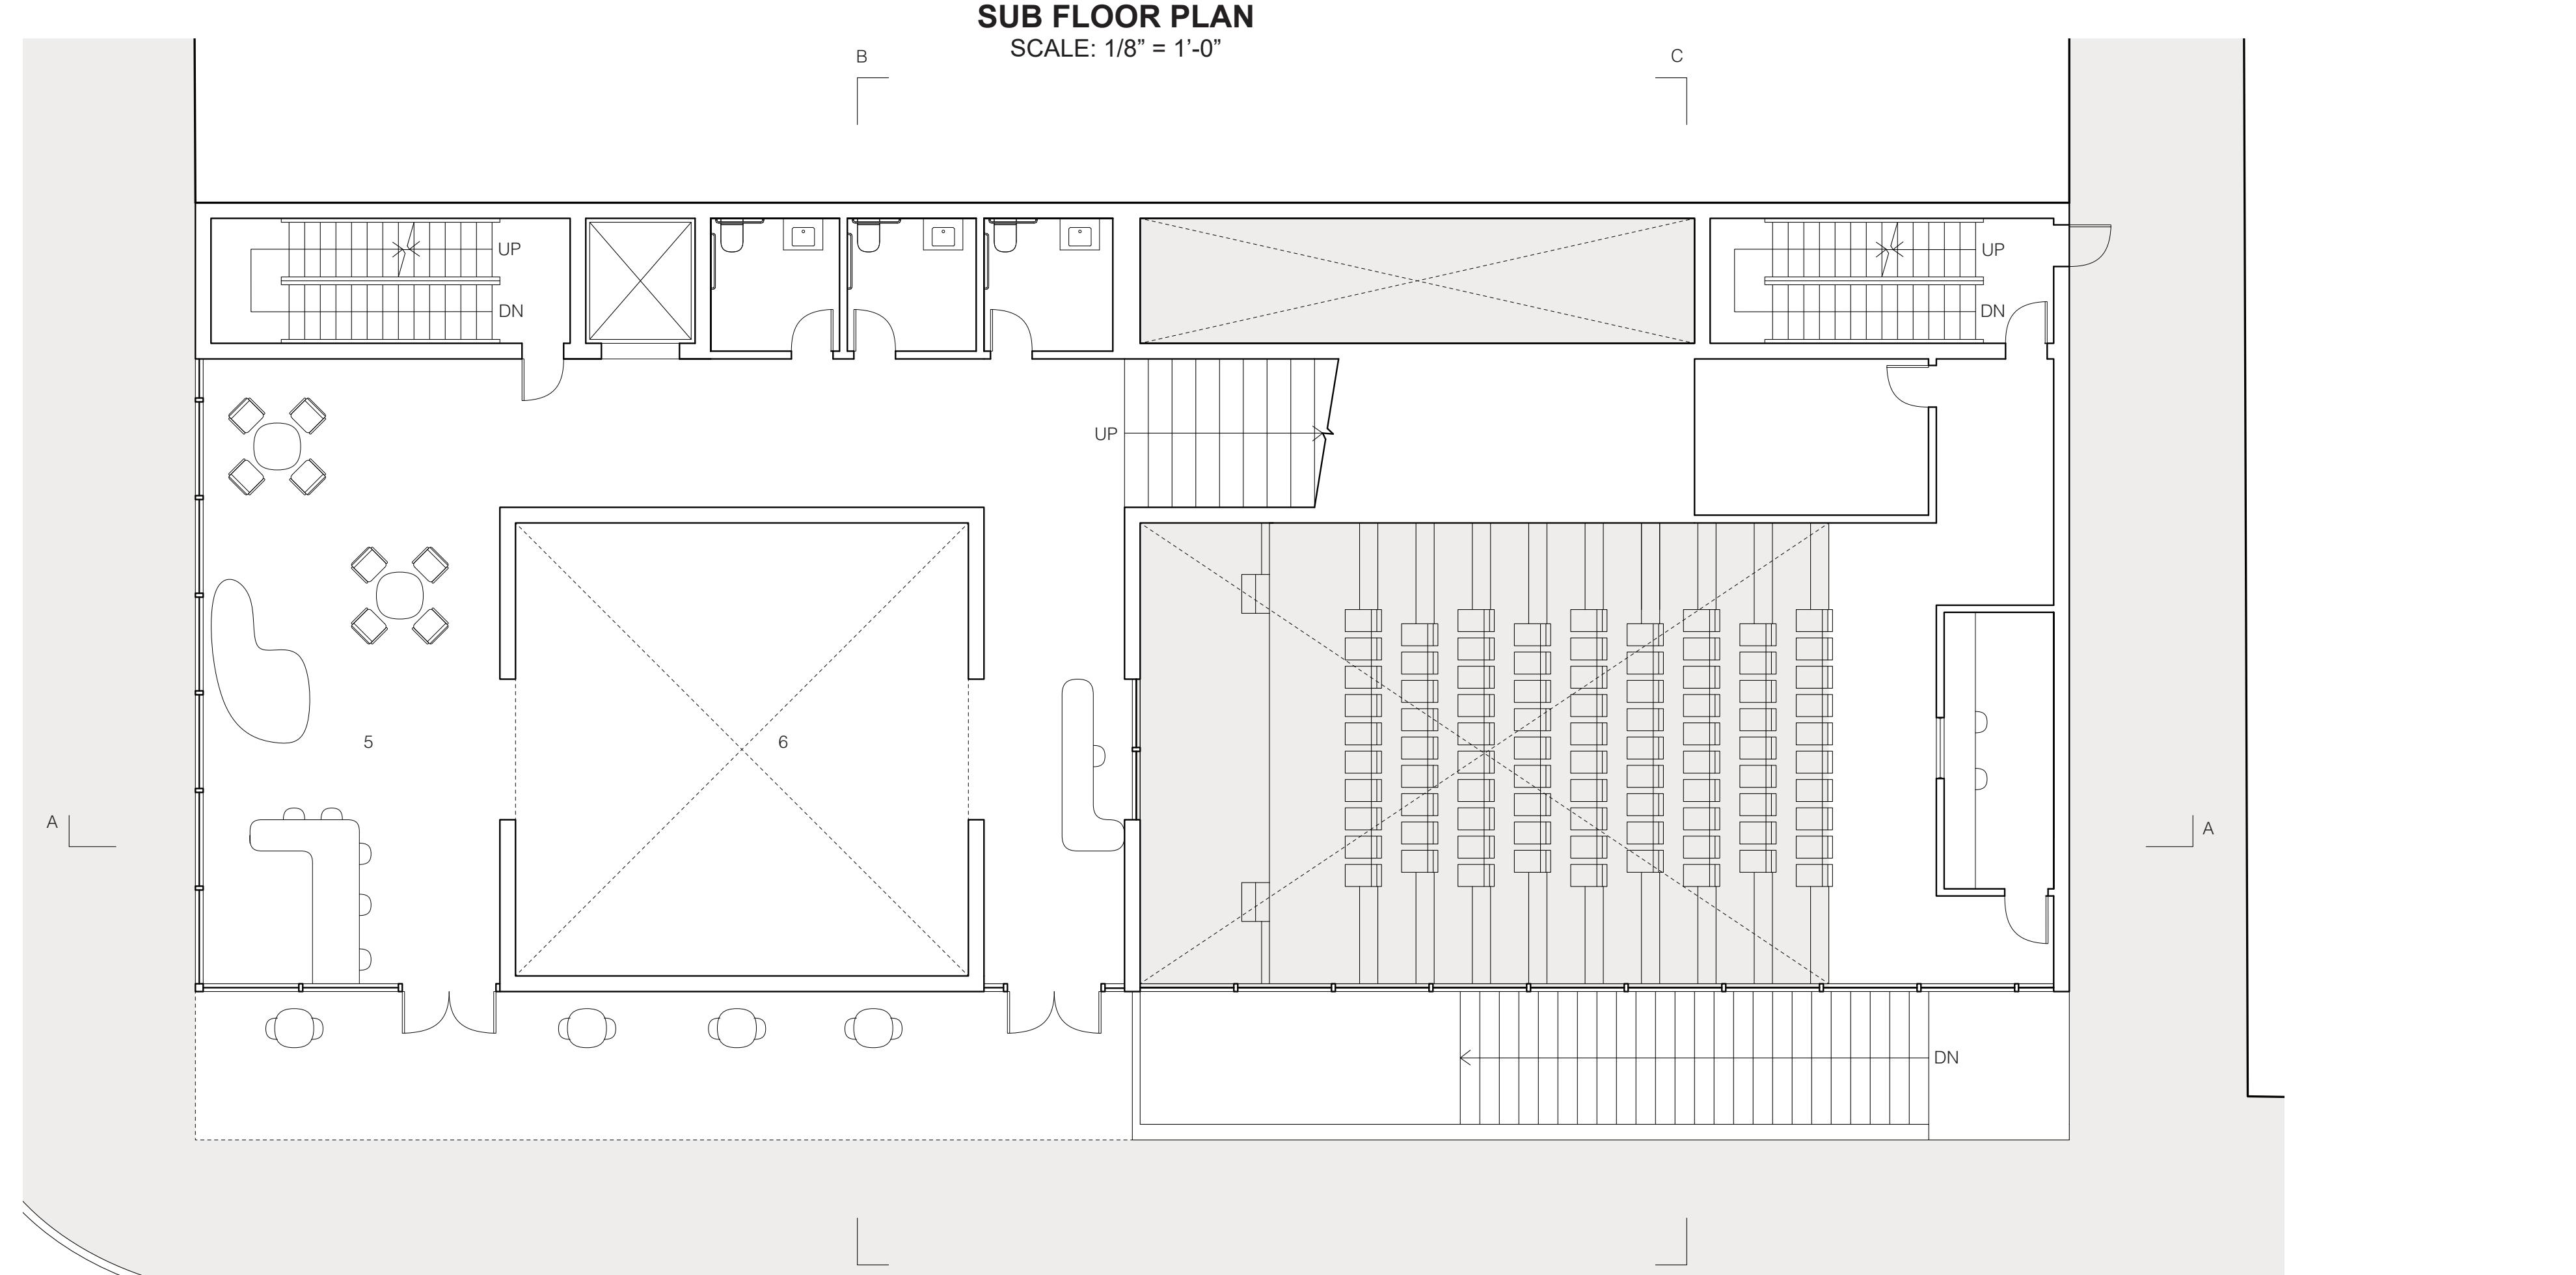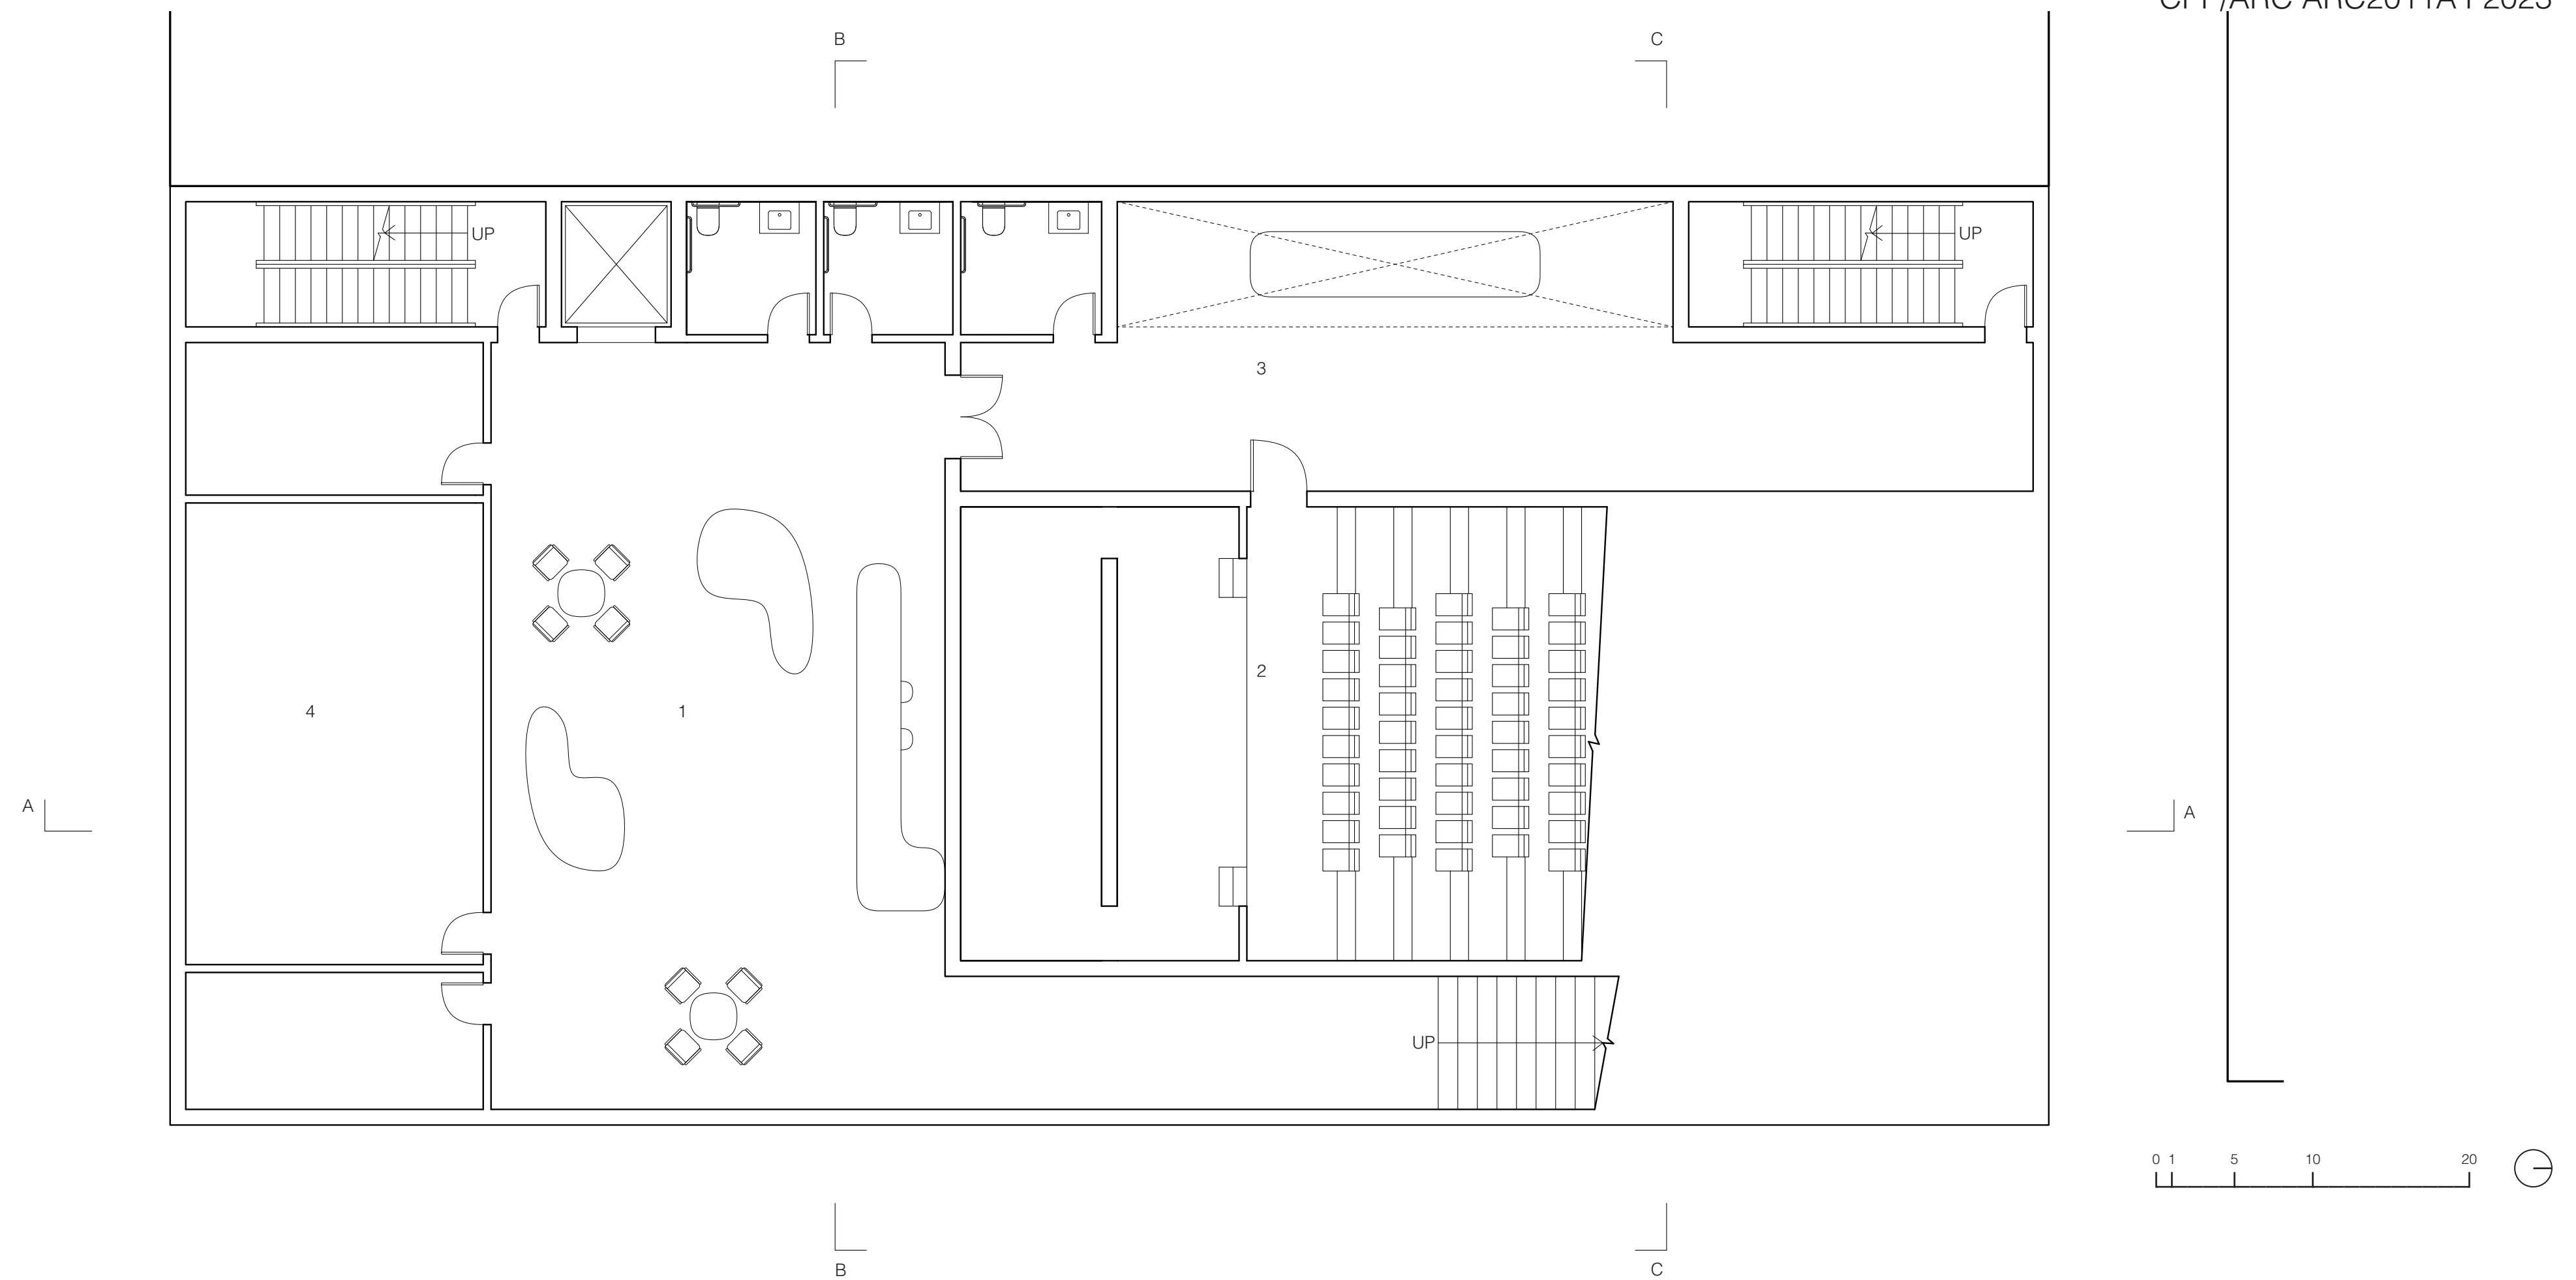

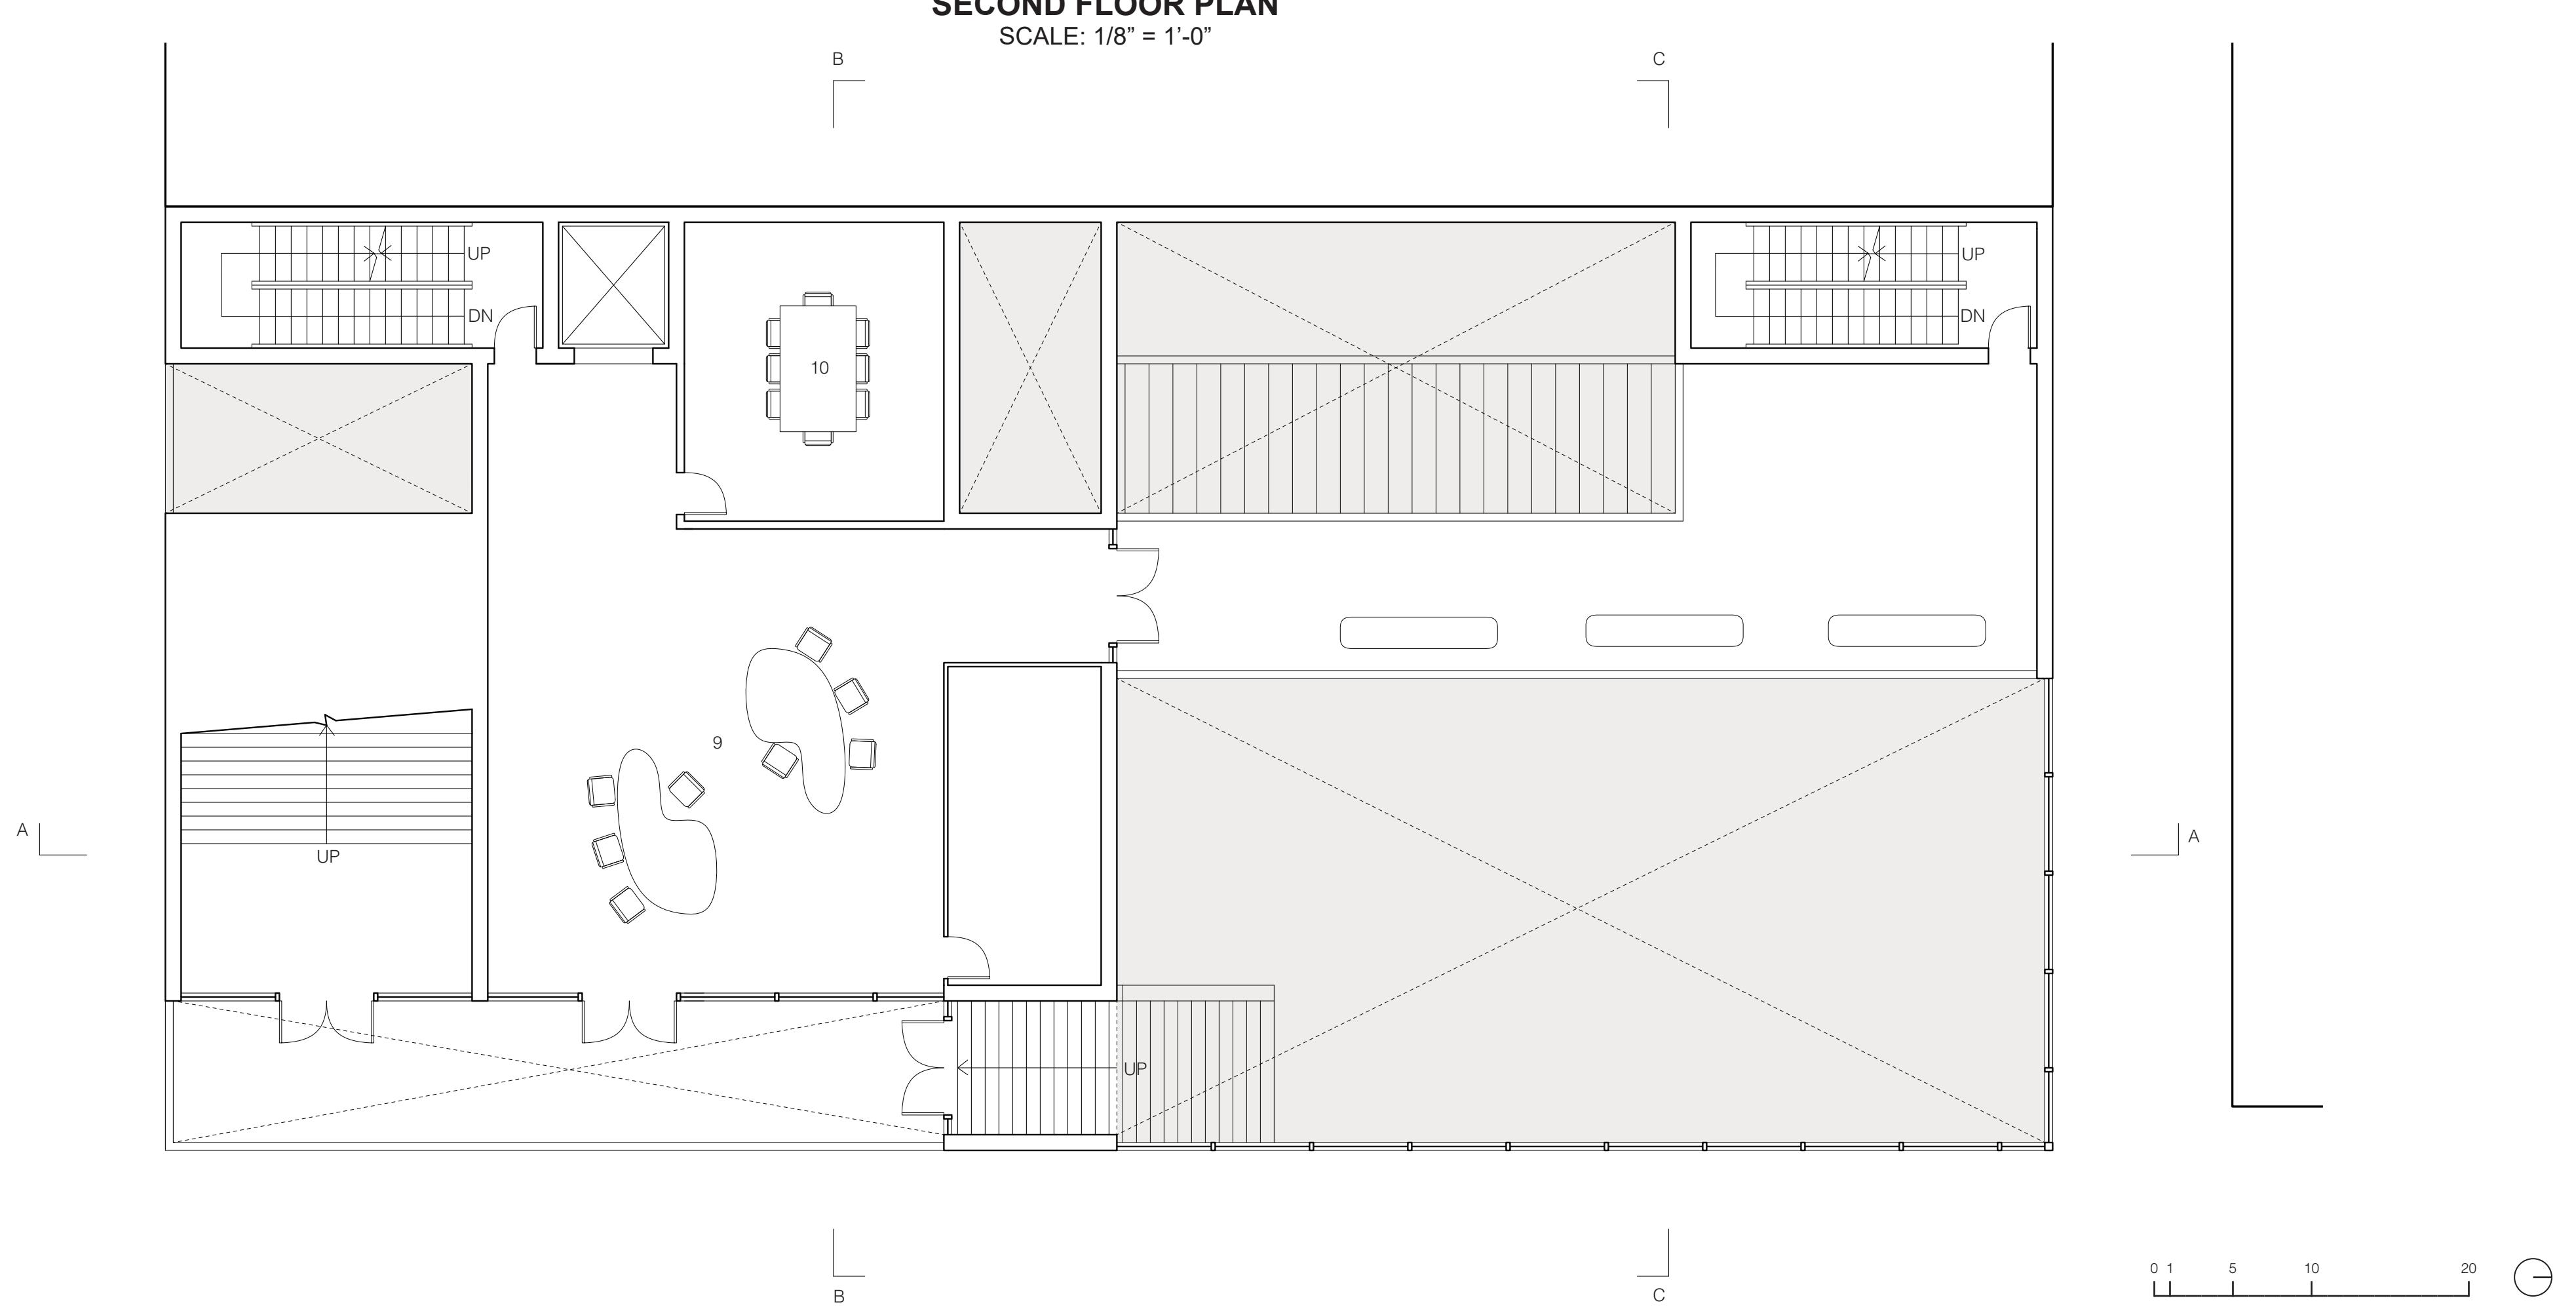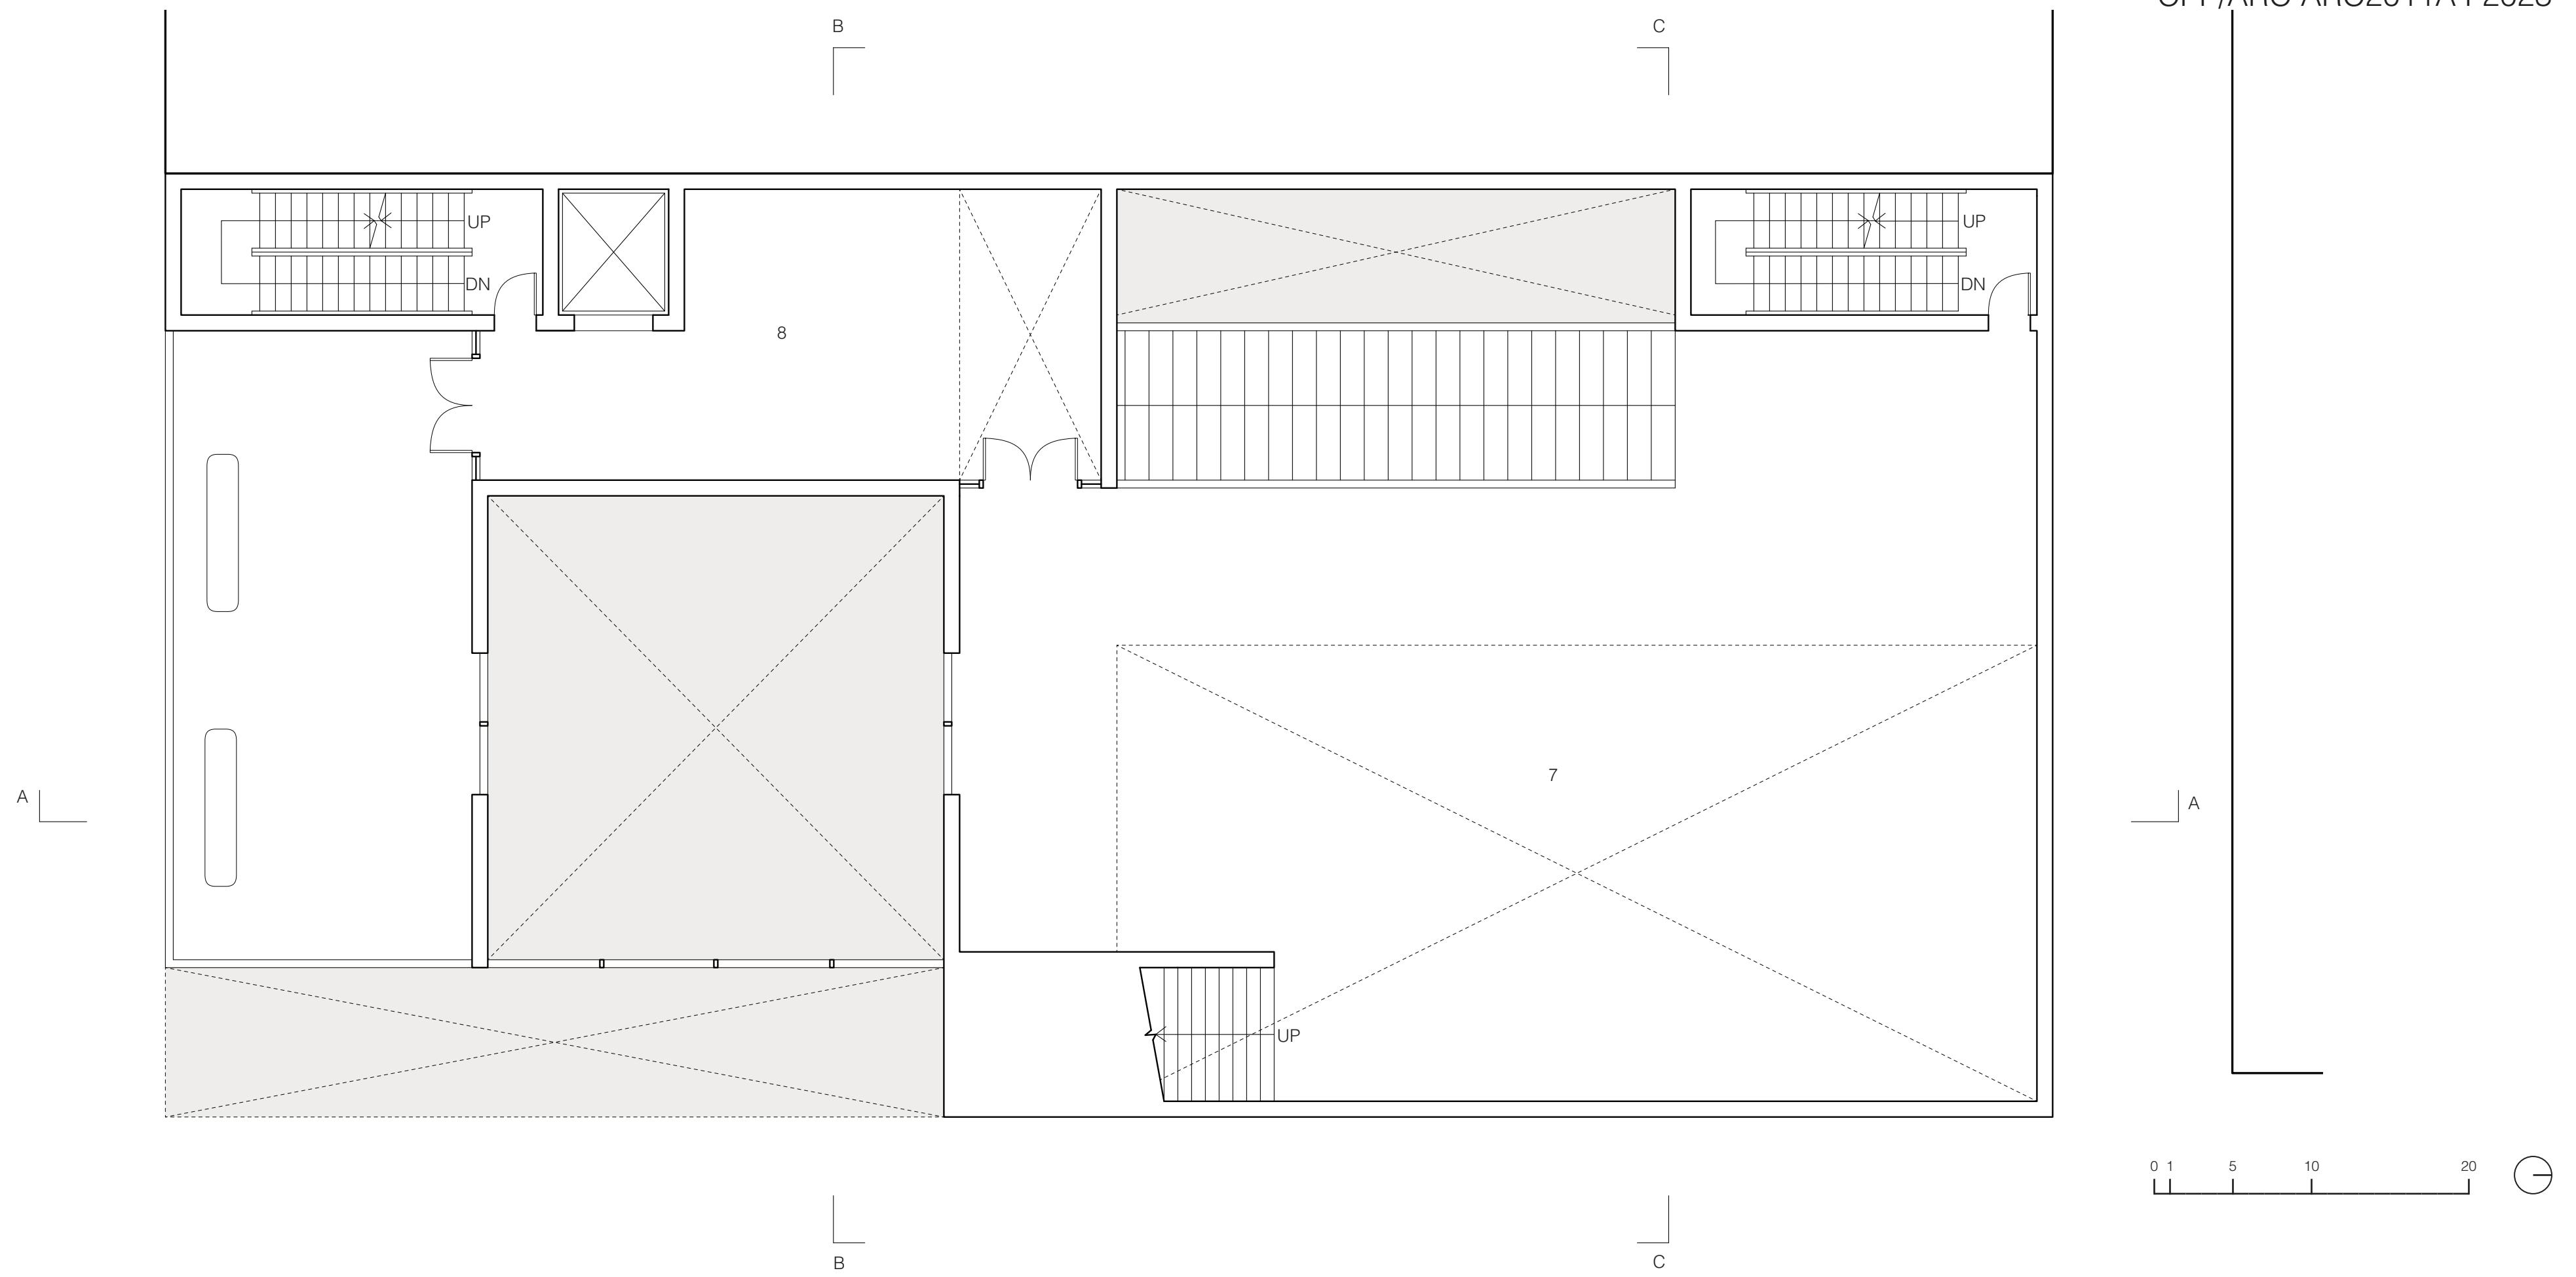


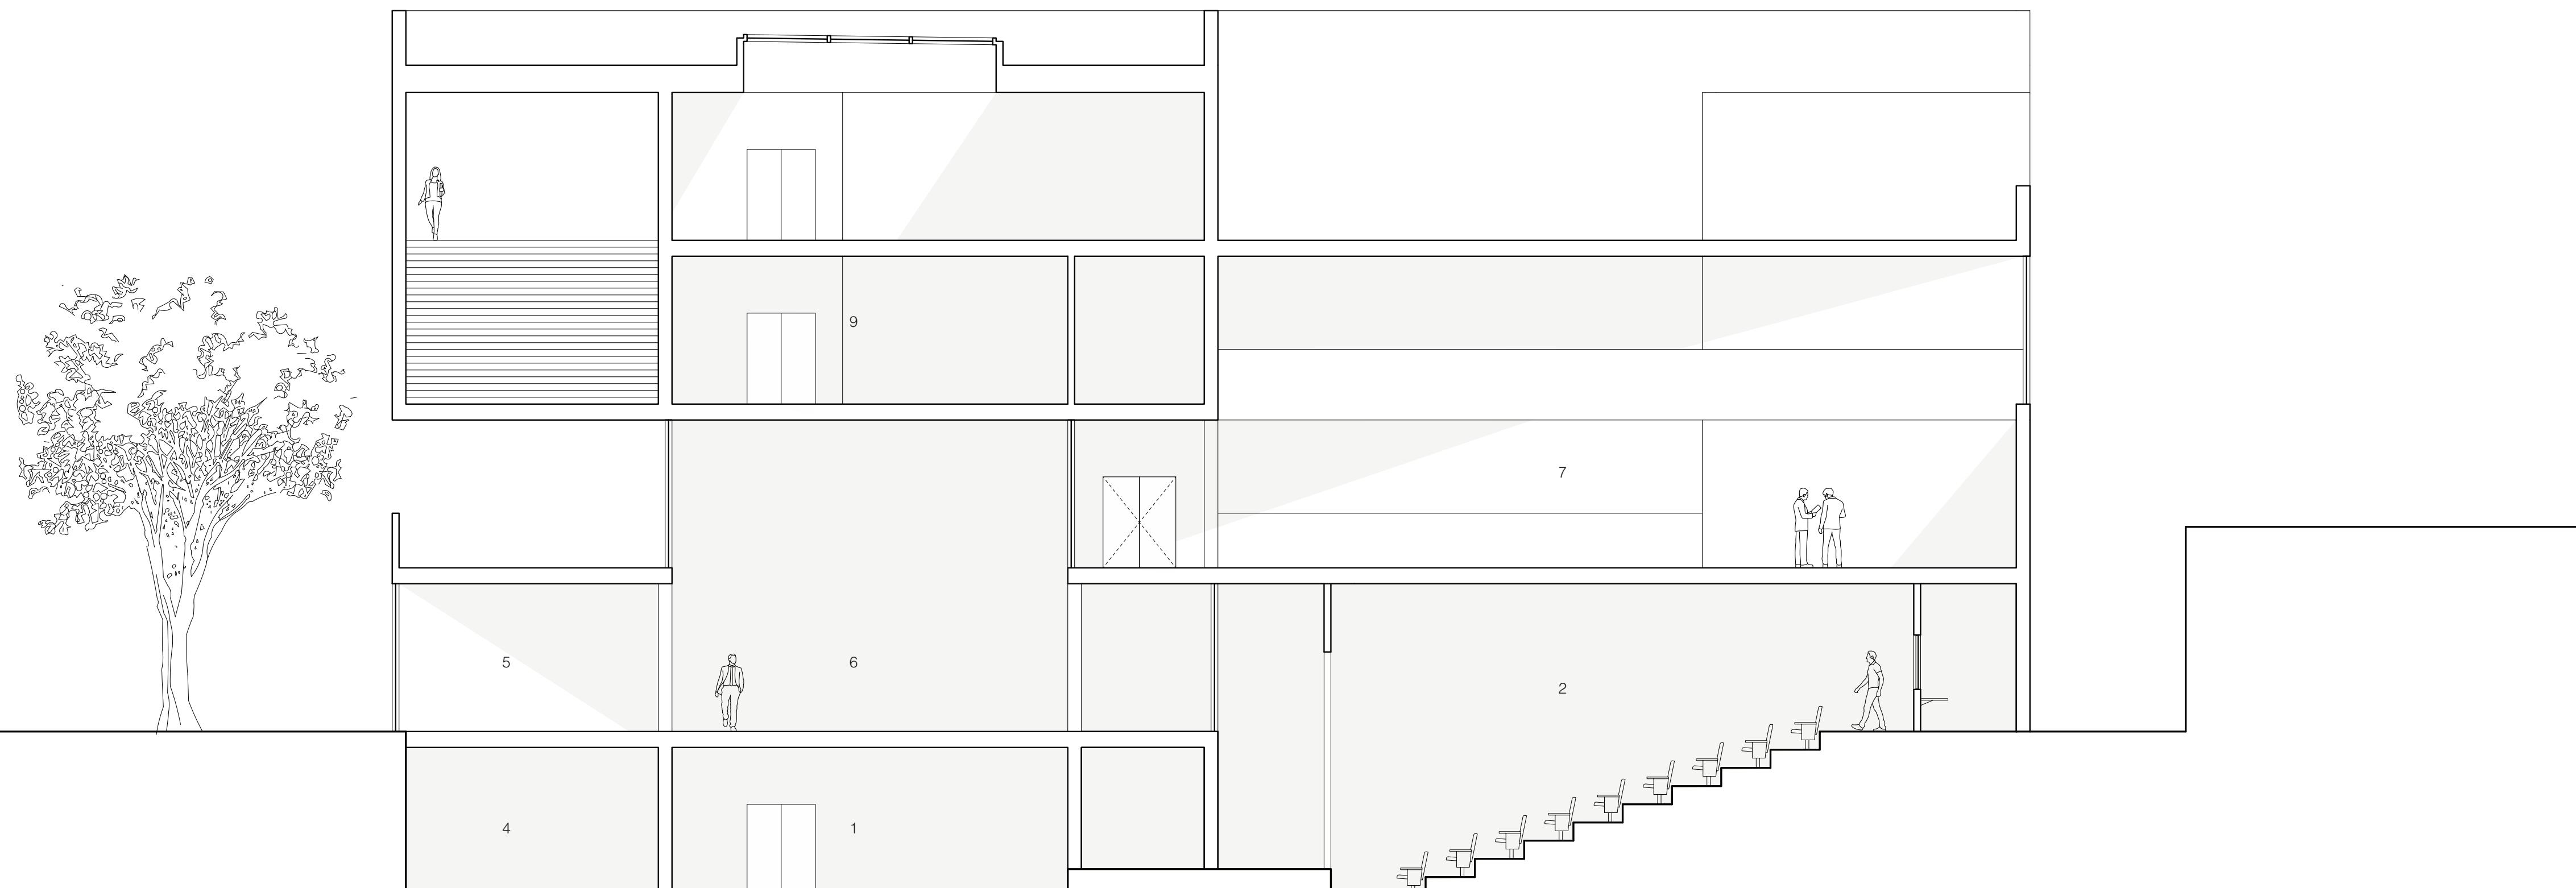

- 1. LOBBY
- 2. AUDITORIUM
- 3. GALLERY 1
- 4. MECHANICAL ROOM
- 5. CAFE/WORKSHOP
- 6. GALLERY 2
- 7. MUSICAL SHOWCASE ROOM
- 8. STORE
- 9. ART WORKSPACE
- 10. CONFERENCE ROOM


0 1 5 10 20

LONGITUDINAL SECTION A
SCALE: 1/8" = 1'-0"

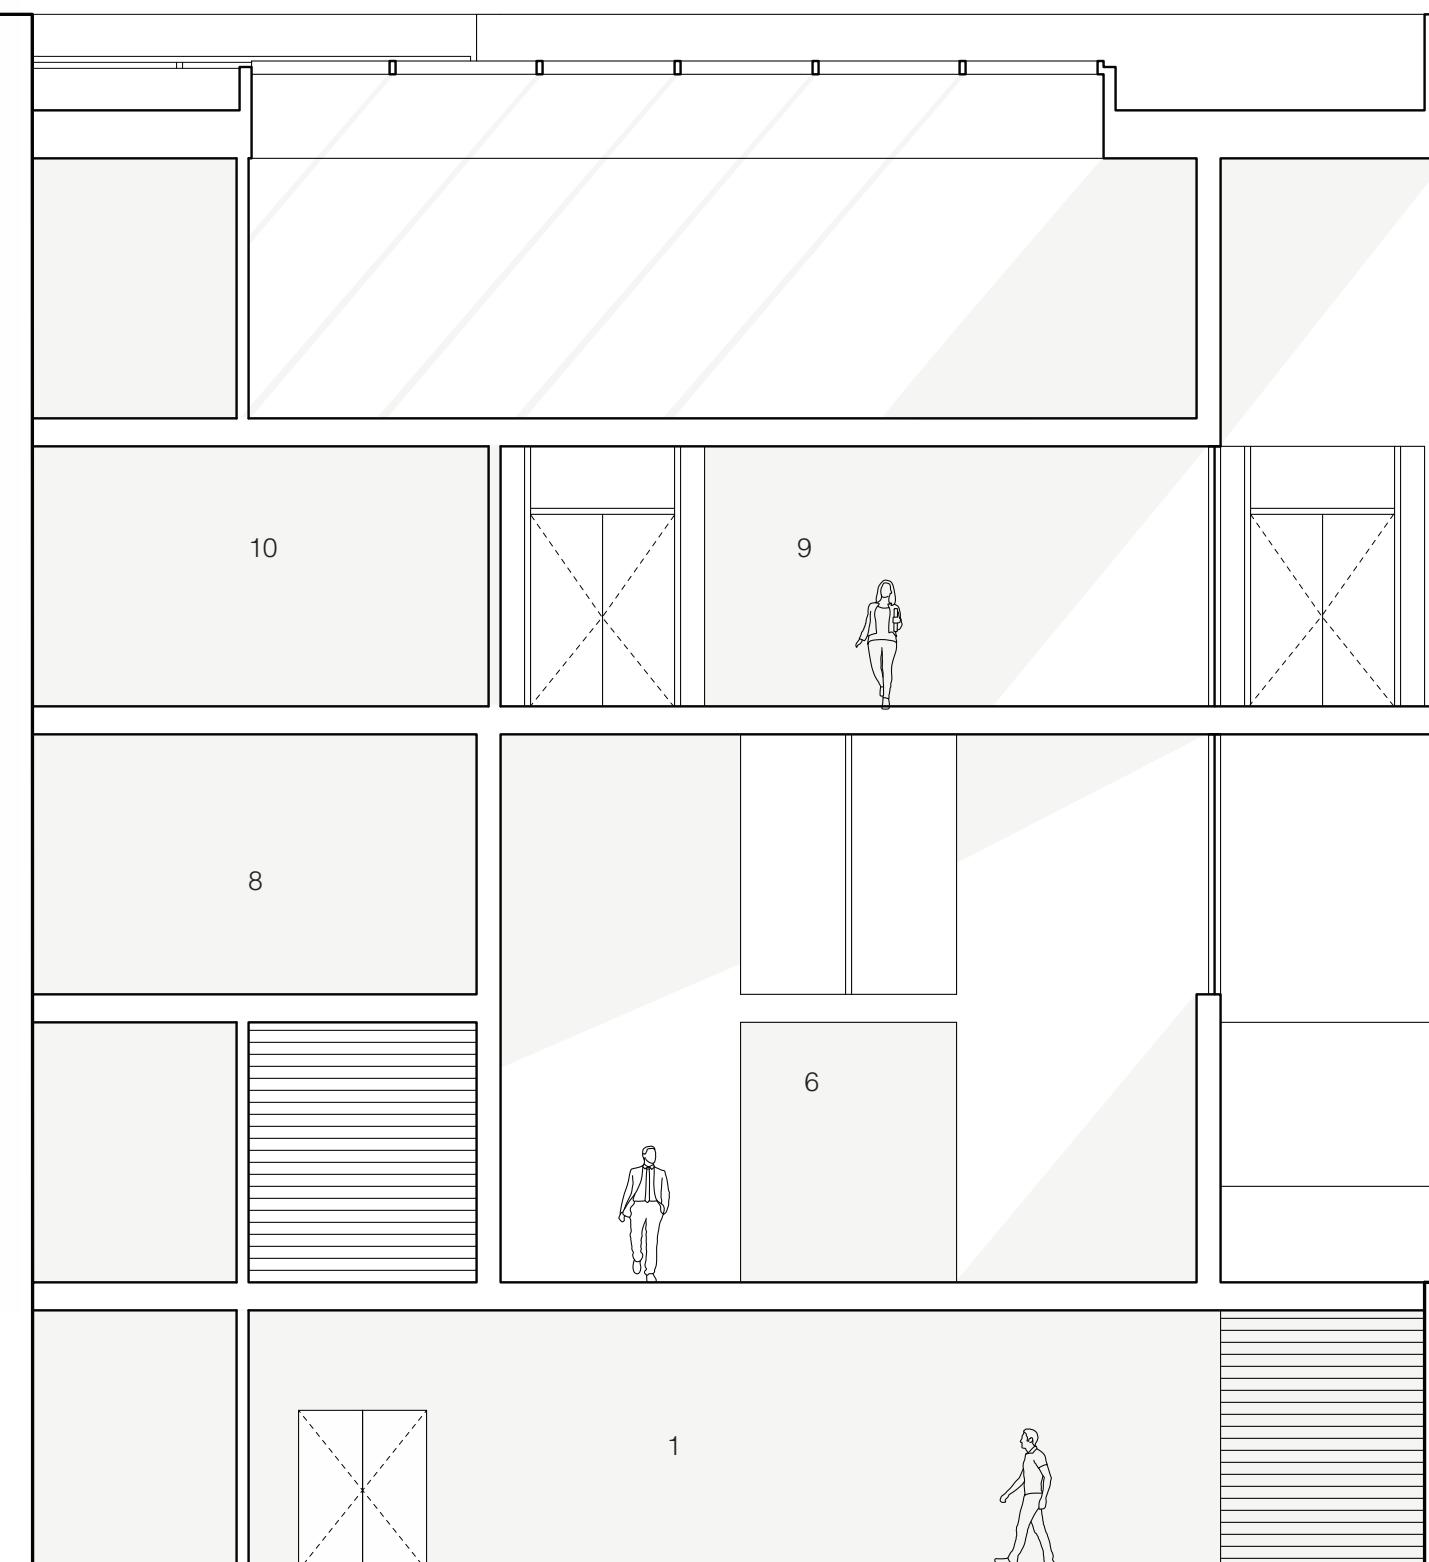

CROSS SECTION B
SCALE: 1/8" = 1'-0"

- 1. LOBBY
- 2. AUDITORIUM
- 3. GALLERY 1
- 4. MECHANICAL ROOM
- 5. CAFE/WORKSHOP
- 6. GALLERY 2
- 7. MUSICAL SHOWCASE ROOM
- 8. STORE
- 9. ART WORKSPACE
- 10. CONFERENCE ROOM

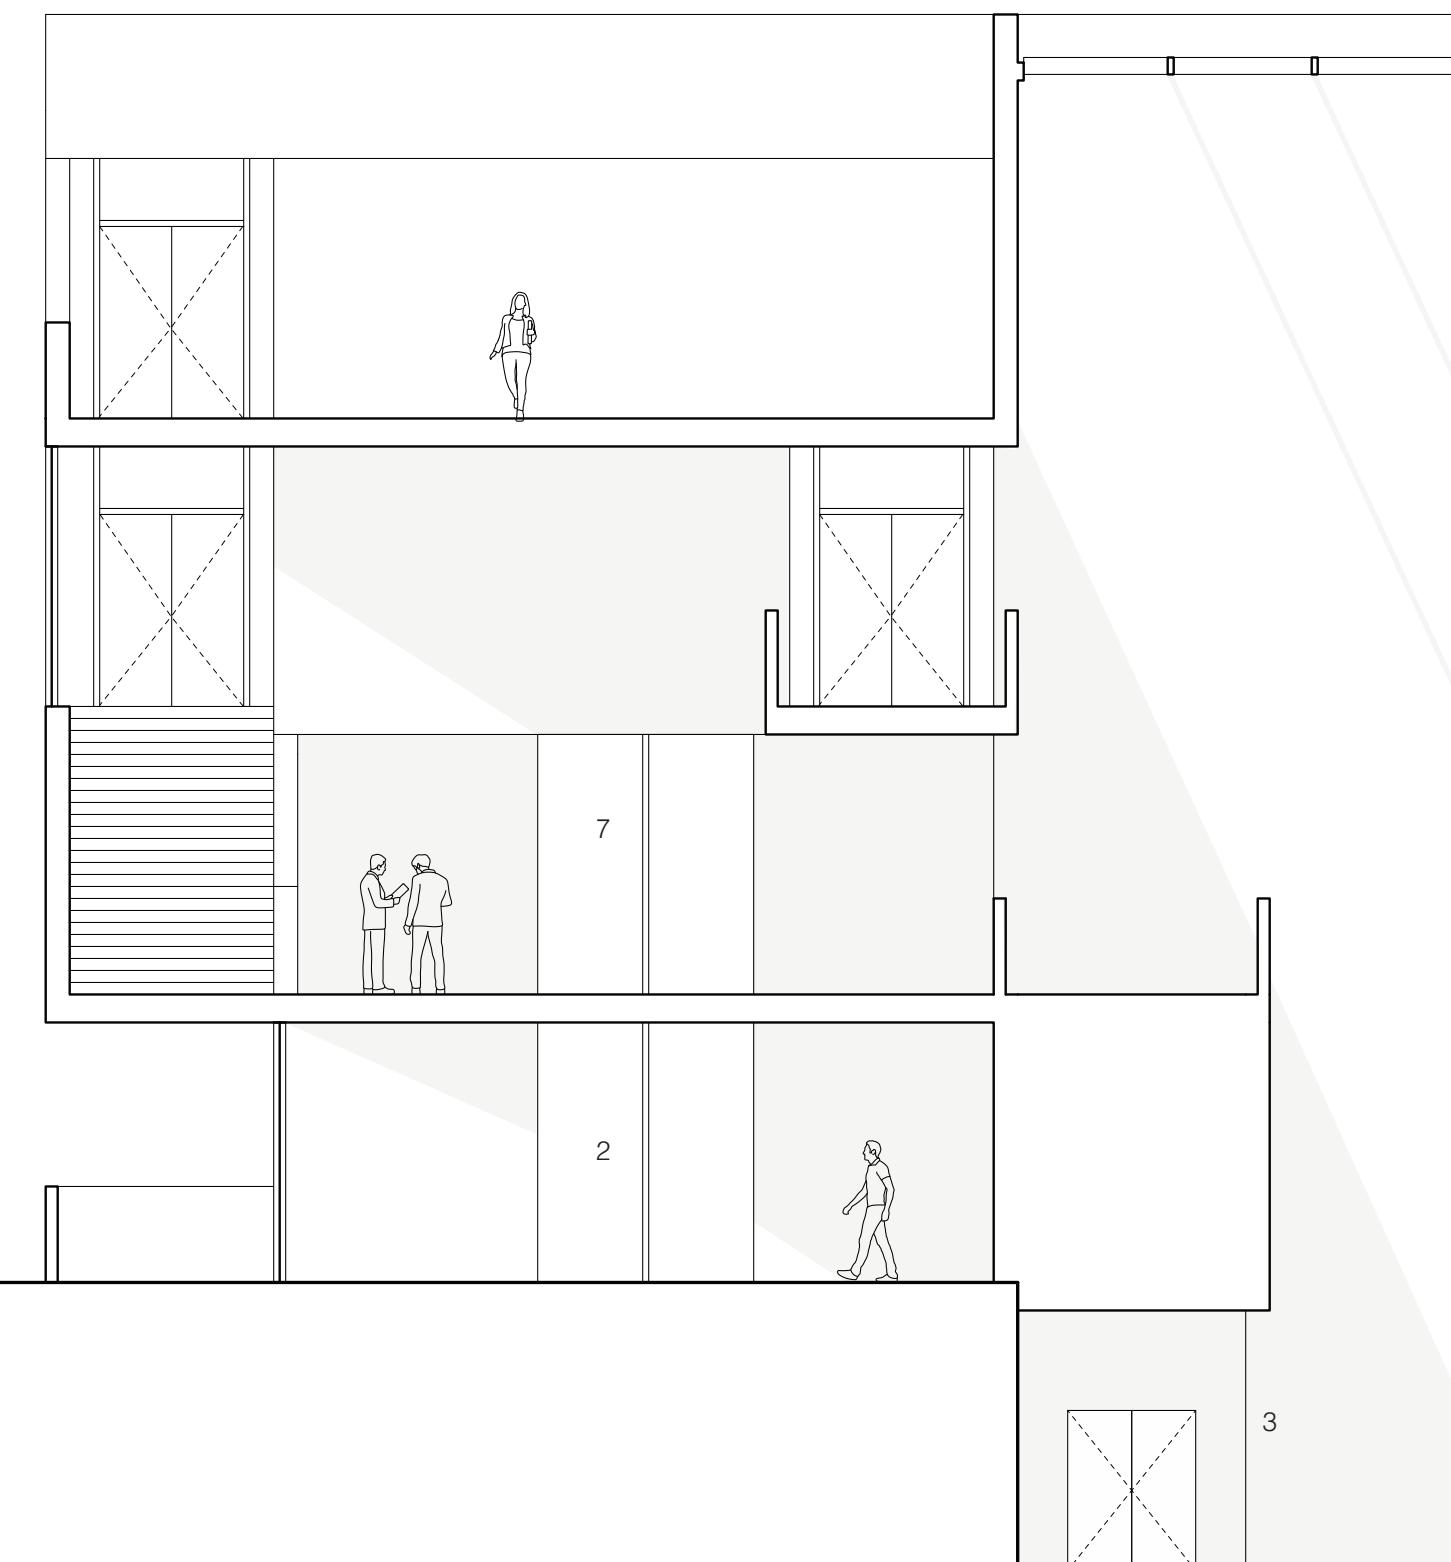

CROSS SECTION C
SCALE: 1/8" = 1'-0"

0 1 5 10 20



(VIEW OF GALLERY 2)



(VIEW OF MUSICAL SHOWCASE ROOM FR ABV)